





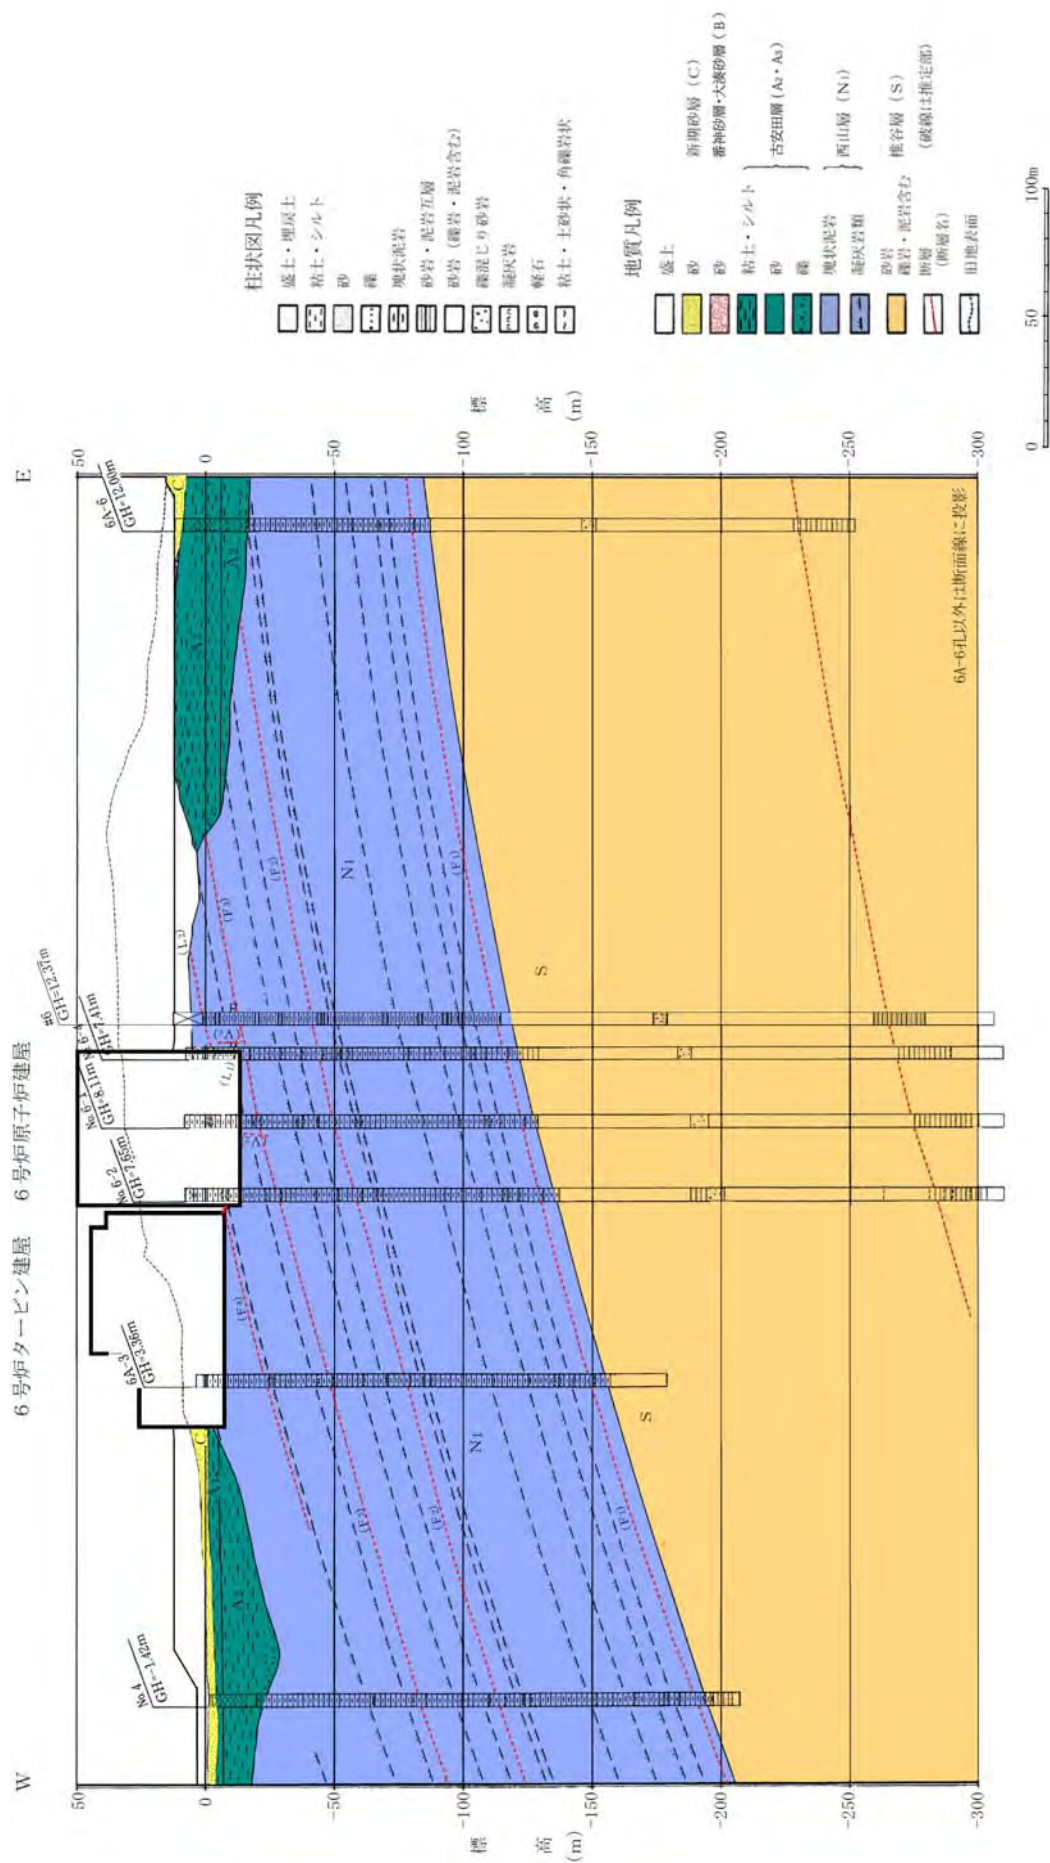


第3.2.6-1図(2) 6号炉付近の地盤分類図






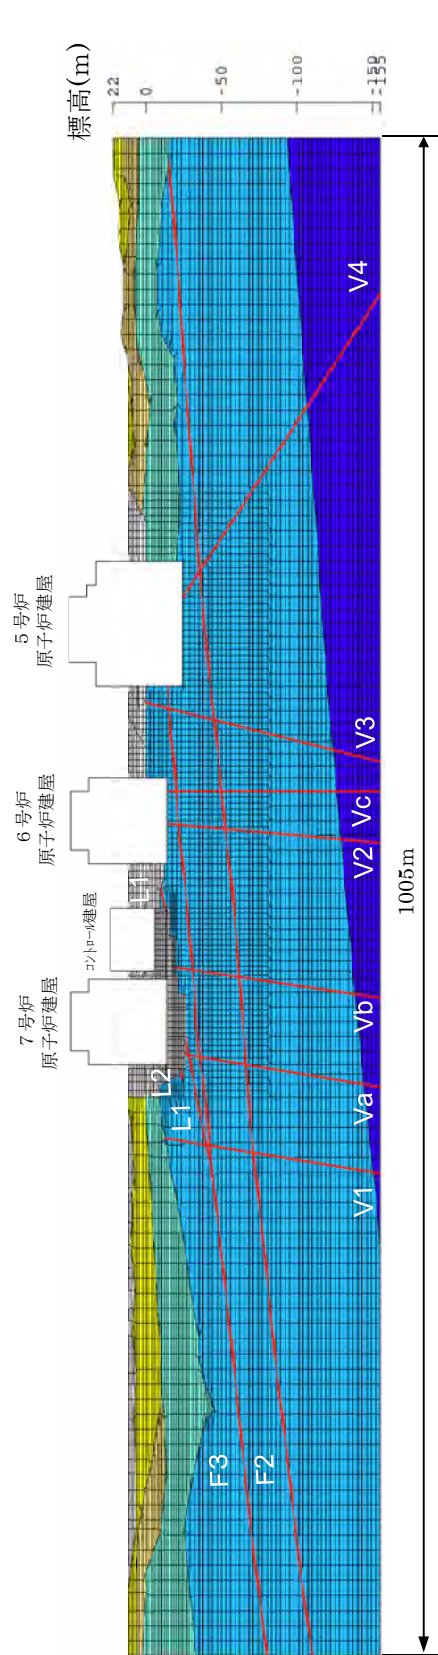


第 3.2.6-2 図(1) 解析用要素分割図 (6・7号炉汀線平行断面)

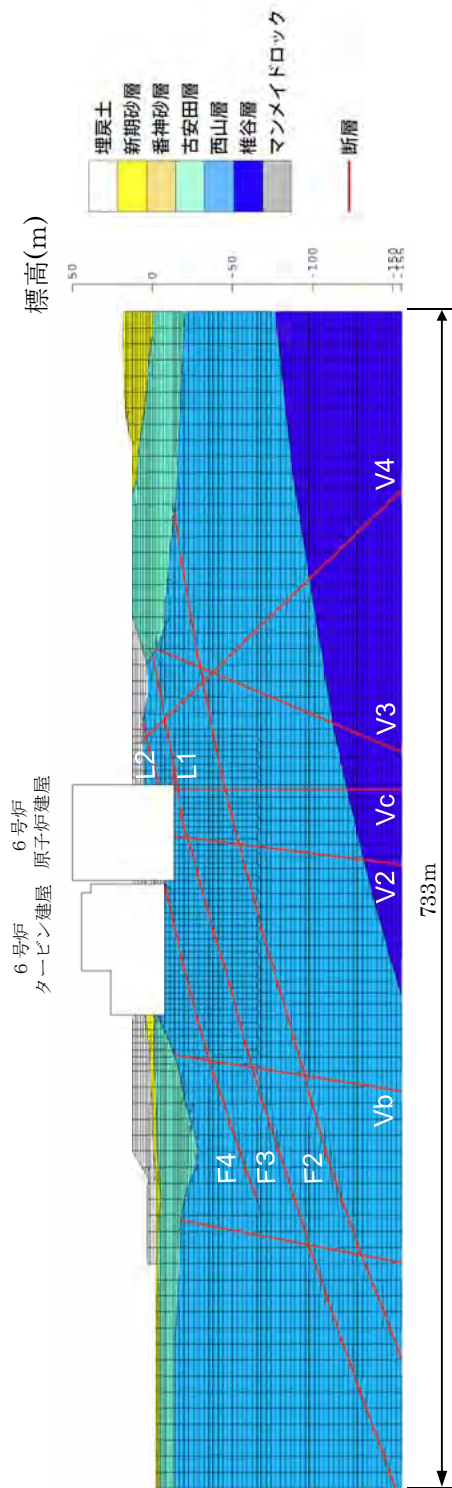

第 3.2.6-2 図(2) 解析用要素分割図 (6号炉汀線直交断面)

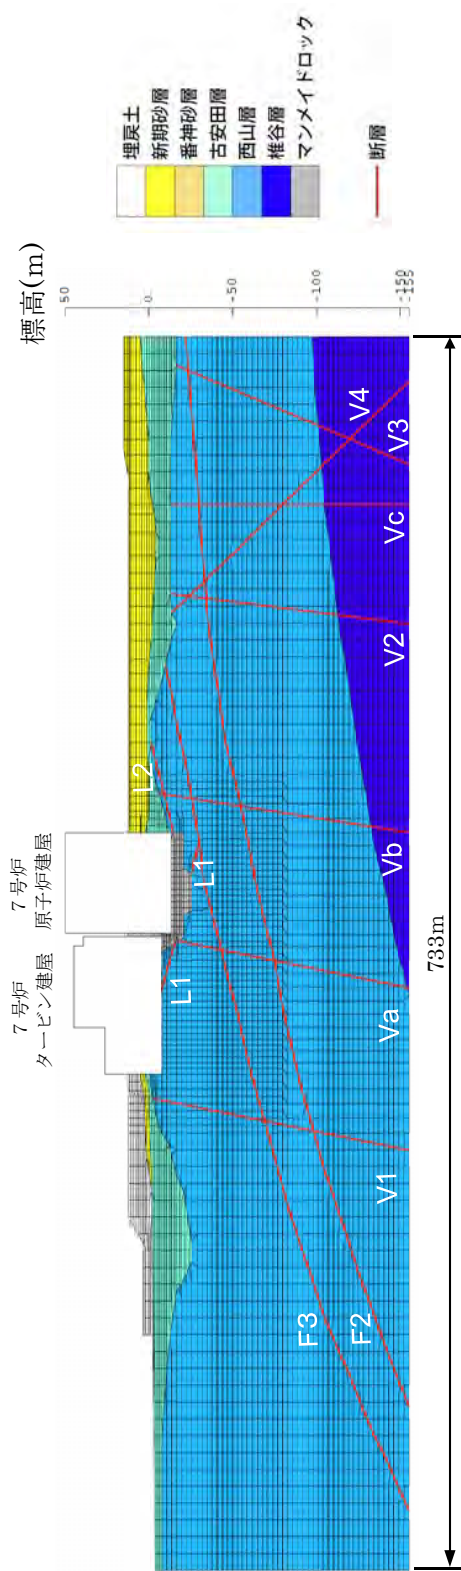

第 3.2.6-2 図(3) 解析用要素分割図 (7号炉汀線直交断面)

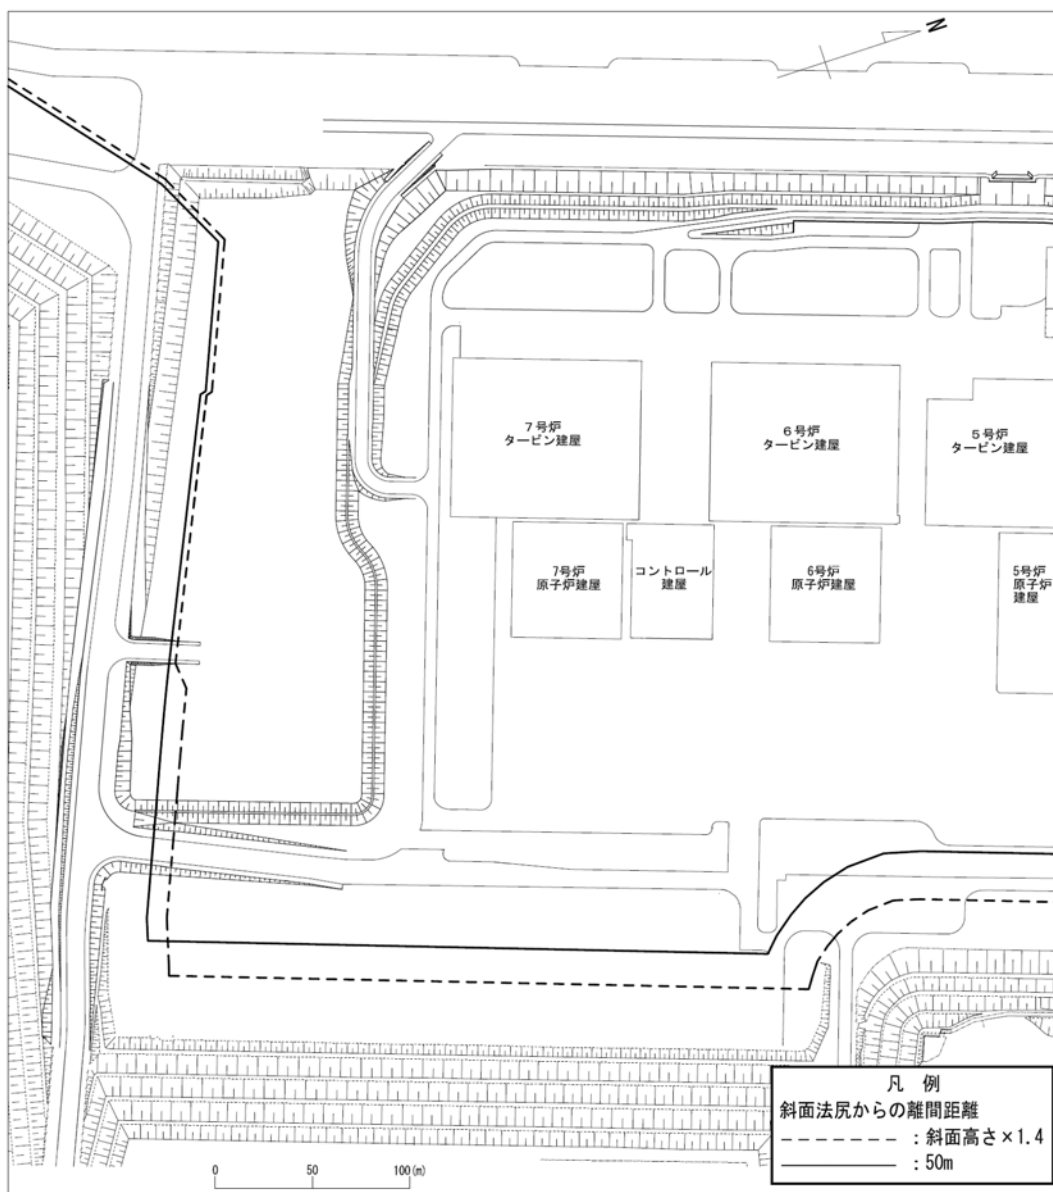

第 3. 2. 6-3 図 6 号及び 7 号炉付近平面図